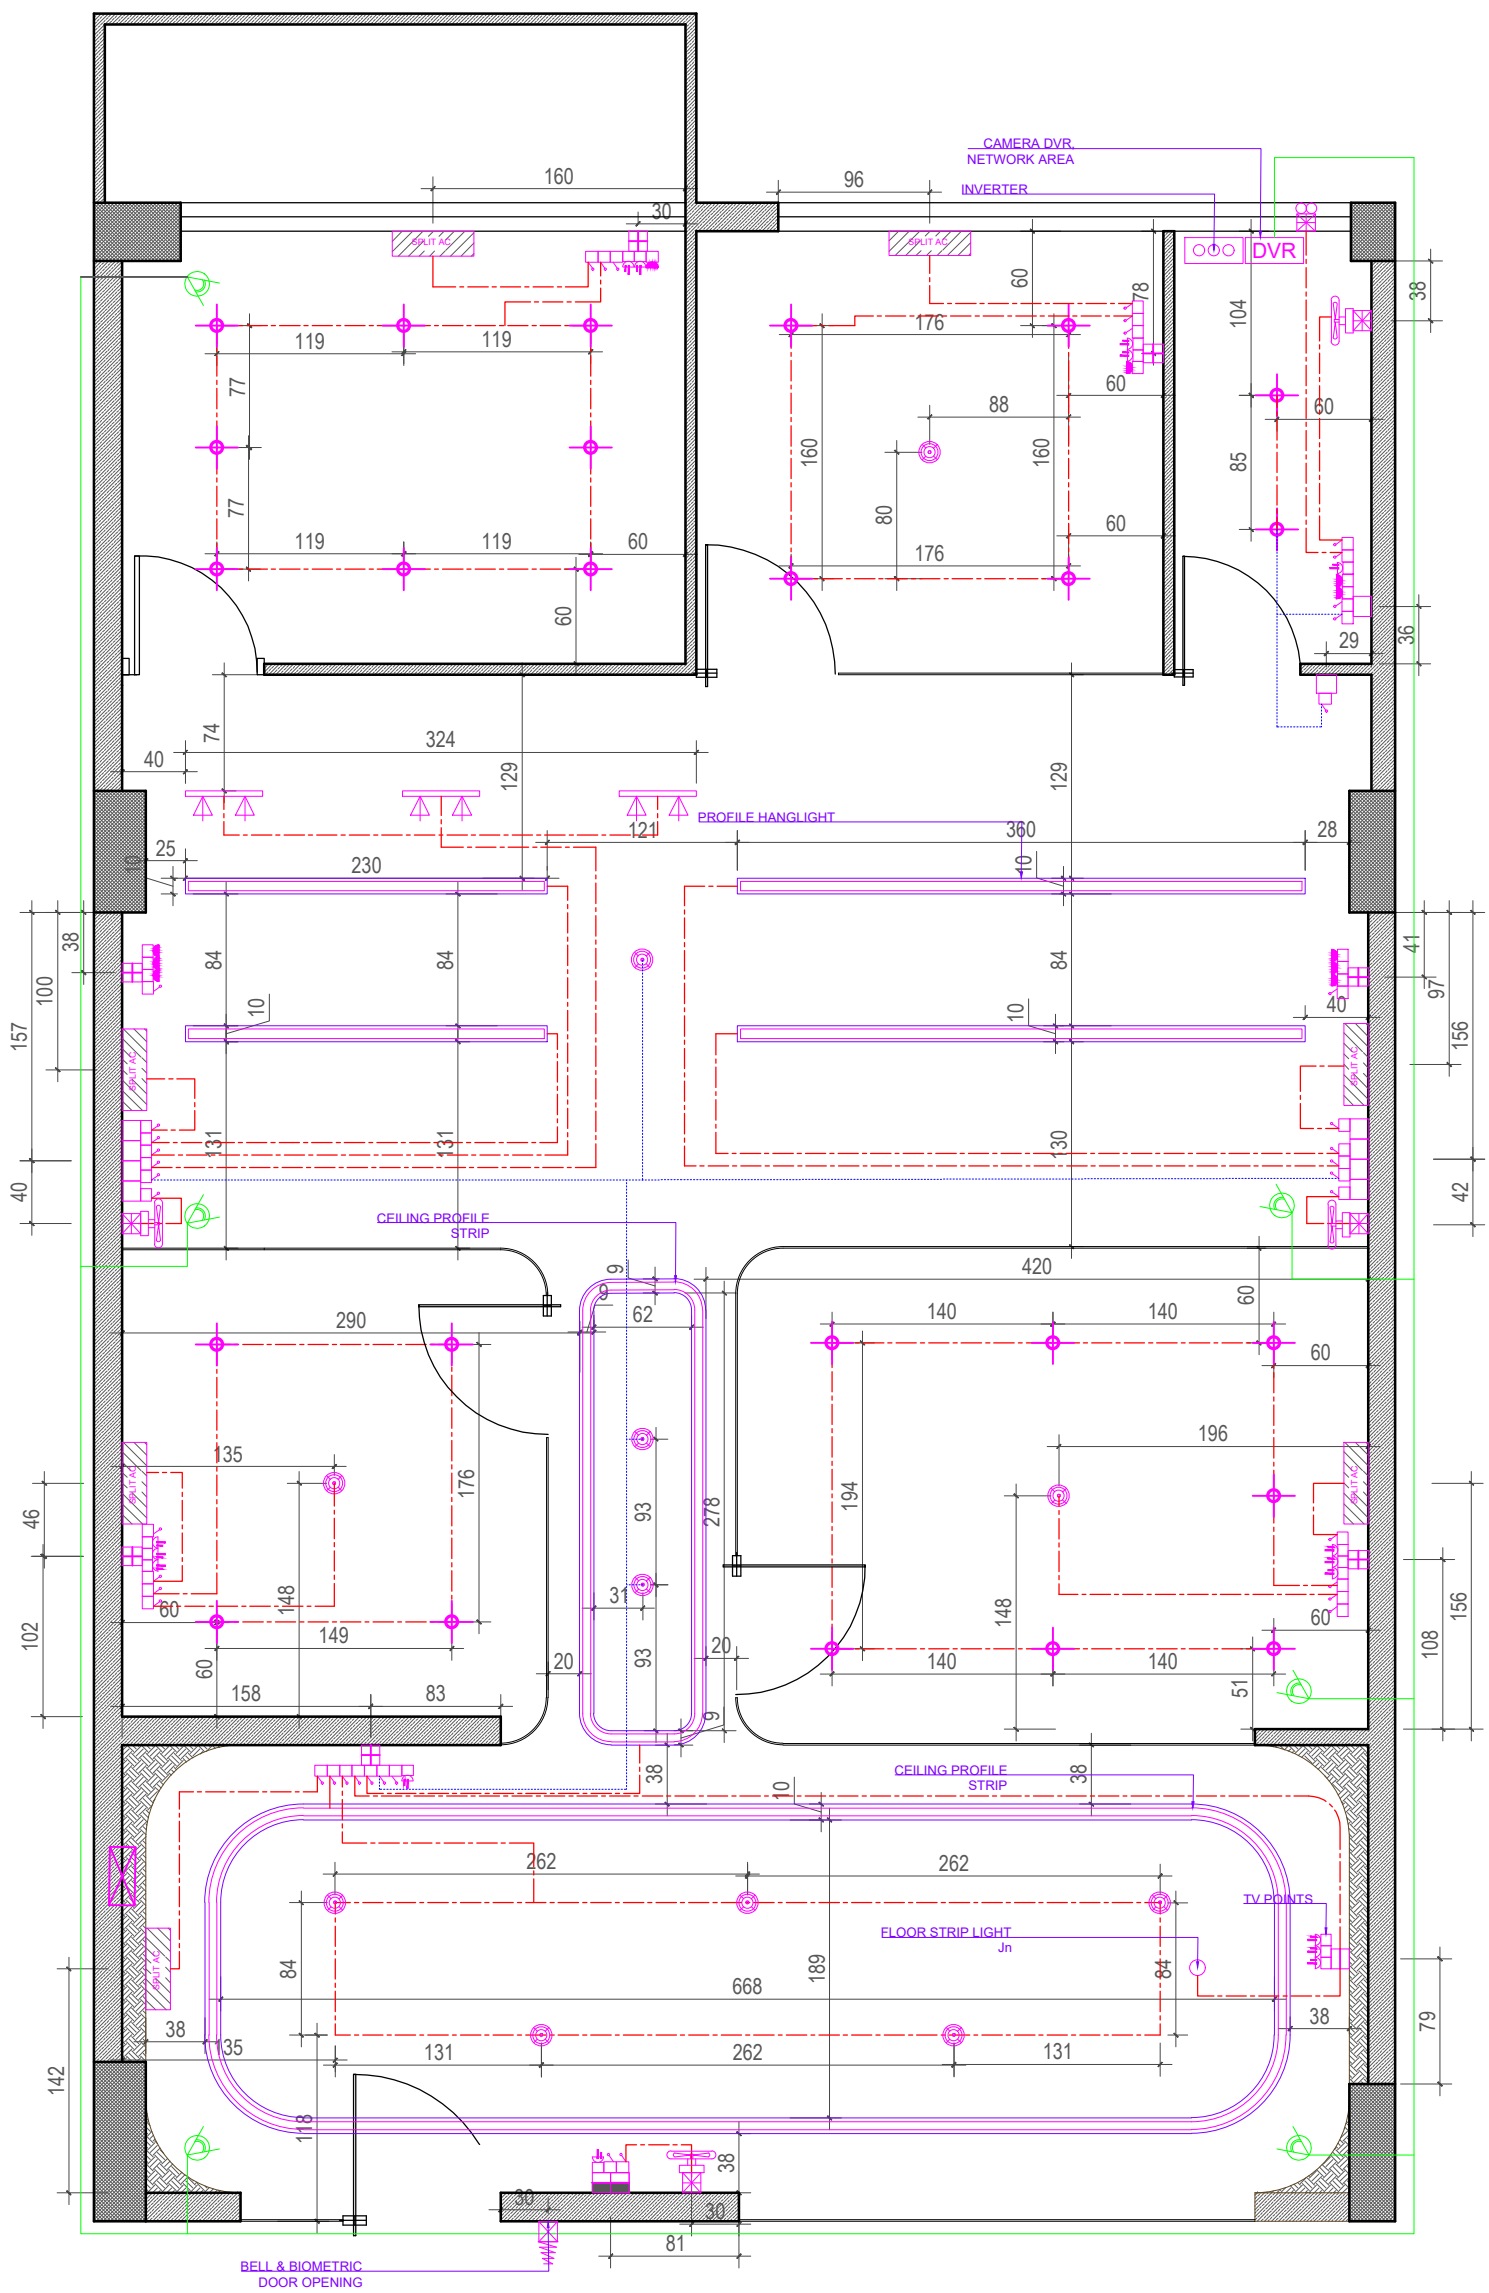

LEGEND	
	WIRE 1(ONE WAY)
	WIRE 2(TWO WAY)
	BED LAMP
	MIRROR LAMP
	PLUG POINT30A - 10 Nos
	SWITCHES - 40 Nos
	2 WAY SWITCHES - 5 Nos
	PLUG POINT 9A - 14 Nos
	PLUG POINT 16A
	FAN
	WALL BRACKET
	CEILING LIGHT
	LED STRIP LIGHT - 36 m
	TRACK LIGHT - 6 Nos
	FLOOR LAMP
	ADJUSTABLE SPOT LIGHT
	SPOT LIGHT - 25 Nos
	ELECTRICAL CHIMNEY
	UP & DOWN LIGHT
	PENDENT LIGHT - 11 Nos
	WALL FAN - 4 Nos
	GEYSER
	BELL SWITCH - 1 Nos
	EXHAUST FAN - 1 Nos
	MAIN BOARD
	DISTRIBUTION BOARD - 1 Nos
	INVERTER - 1 Nos
	TUBE LIGHT
	CHANDELIER
	CCTV CAMERA - 6 Nos
	SPLIT AC - 7 Nos
	CABINET LIGHT
WALL HUNG	FOOT LAMP
WALL HUNG	BULK HEAD

SOCKET SWITCHES AT LEVELS			
	140 CM		90 CM
	120 CM		20 CM
	60 CM		210 CM
	150 CM		180 CM
	90 CM		240 CM

LEVELS TAKEN AT TOP OF METAL BOX

NOTES :-

* ALL MEASUREMENTS ARE IN CM UNLESS OTHERWISE SPECIFIED
* DRAWINGS NOT TO BE SCALED
* DRAWINGS TO BE READ IN CONJUNCTION AND RELEVANT ARCHITECTURAL DRAWINGS

PROJECT
KINFRA OFFICE

INTERIOR DESIGNERS
ARCHITECTURE NEXT

STRUCTURAL CONSULTANTS

MEP CONSULTANTS

TITLE
ELECTRICAL DRAWING

CLIENT
ABID

DWG NO. :

SHEET NAME :
A3

N

Architecture Next

THIS DRAWING IS COPYRIGHT PROTECTED. IT IS THE PROPERTY OF **ARCHITECTURE NEXT.** IT IS NOT TO BE REPRODUCED, COPIED, HANDED OVER TO A THIRD PARTY OR USED FOR ANY PURPOSE OTHER THAN THAT FOR WHICH IT HAS BEEN LOANED.

DRN. : KETH

DATE : 18.02.2026

CKD. : NAP

SCALE : NTS