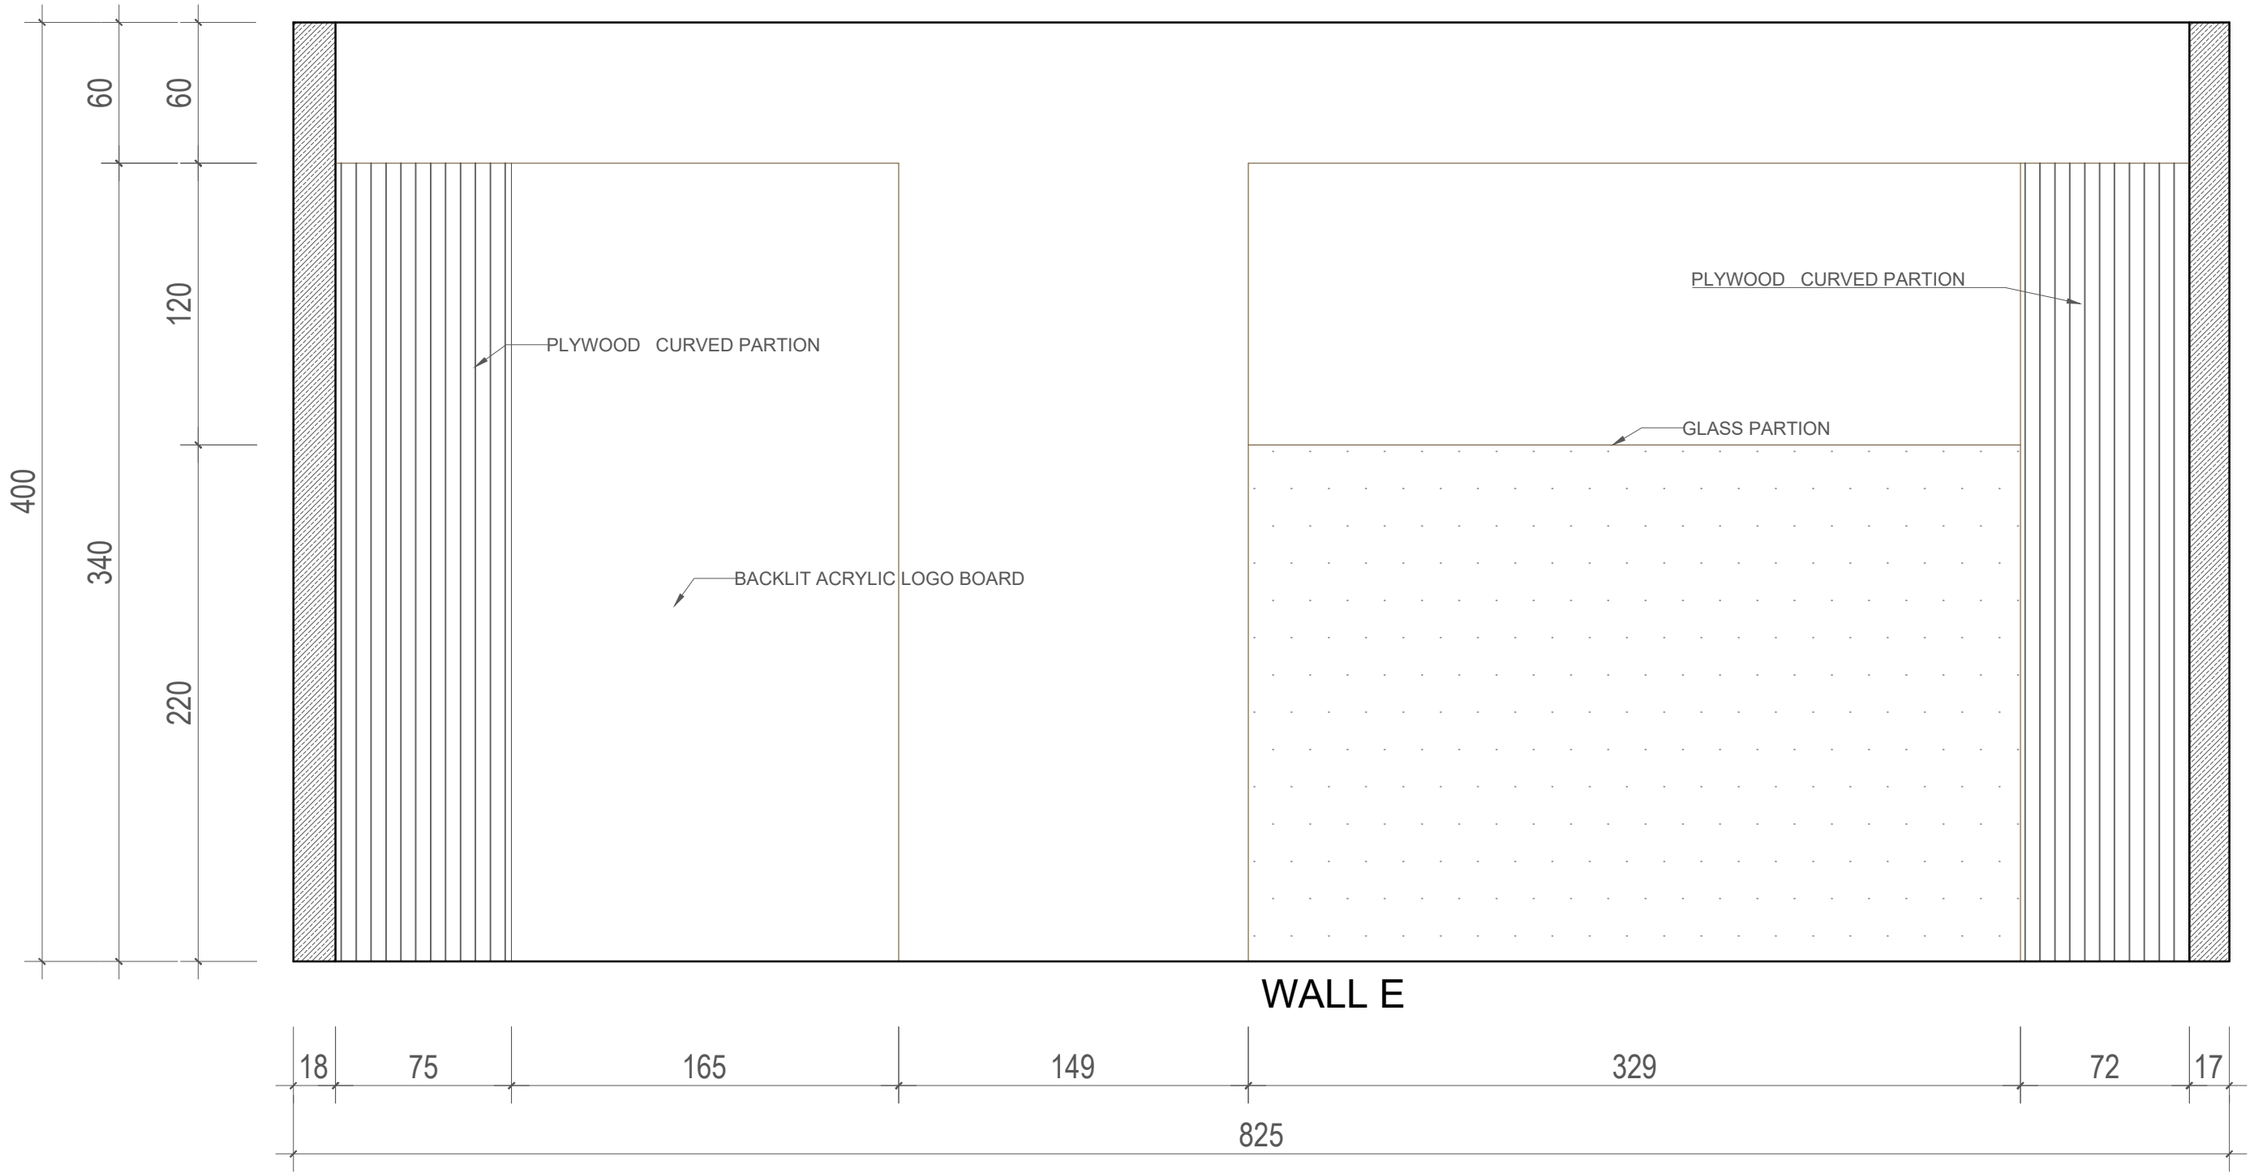

REVISIONS			
NO.	DATE	DESCRIPTION	CHK

NOTES :

AREA DETAILS

FLOOR AREA	: 190.26 SQM (2047.9 SQFT)
CARPET AREA	: 169.86 SQM (1828.3 SQFT)
WALL	: 23 CM

PROJECT **G9 KINFRA OFFICE**

INTERIOR DESIGNERS
ARCHITECTURE NEXT ●

STRUCTURAL CONSULTANTS ○

MEP CONSULTANTS ○

TITLE **WALL E**

CLIENT ABID

DWG NO. :

A4 LANDSCAPE

N

NOTES :-
* ALL MEASUREMENTS ARE IN CM UNLESS OTHERWISE SPECIFIED
* DRAWINGS NOT TO BE SCALED
* DRAWINGS TO BE READ IN CONJUNCTION AND RELEVANT ARCHITECTURAL DRAWINGS

Architecture Next
FIRST FLOOR | HILITE BUSINESS PARK | CALICUT |9995145694

THIS DRAWING IS COPYRIGHT PROTECTED. IT IS THE PROPERTY OF **ARCHITECTURE NEXT.** IT IS NOT TO BE REPRODUCED, COPIED, HANDED OVER TO A THIRD PARTY OR USED FOR ANY PURPOSE OTHER THAN THAT FOR WHICH IT HAS BEEN LOANED.

DRN. : KETH

CKD. : NAP

DATE : 05.03.2026

SCALE : NTS

+91 9995 1456 94