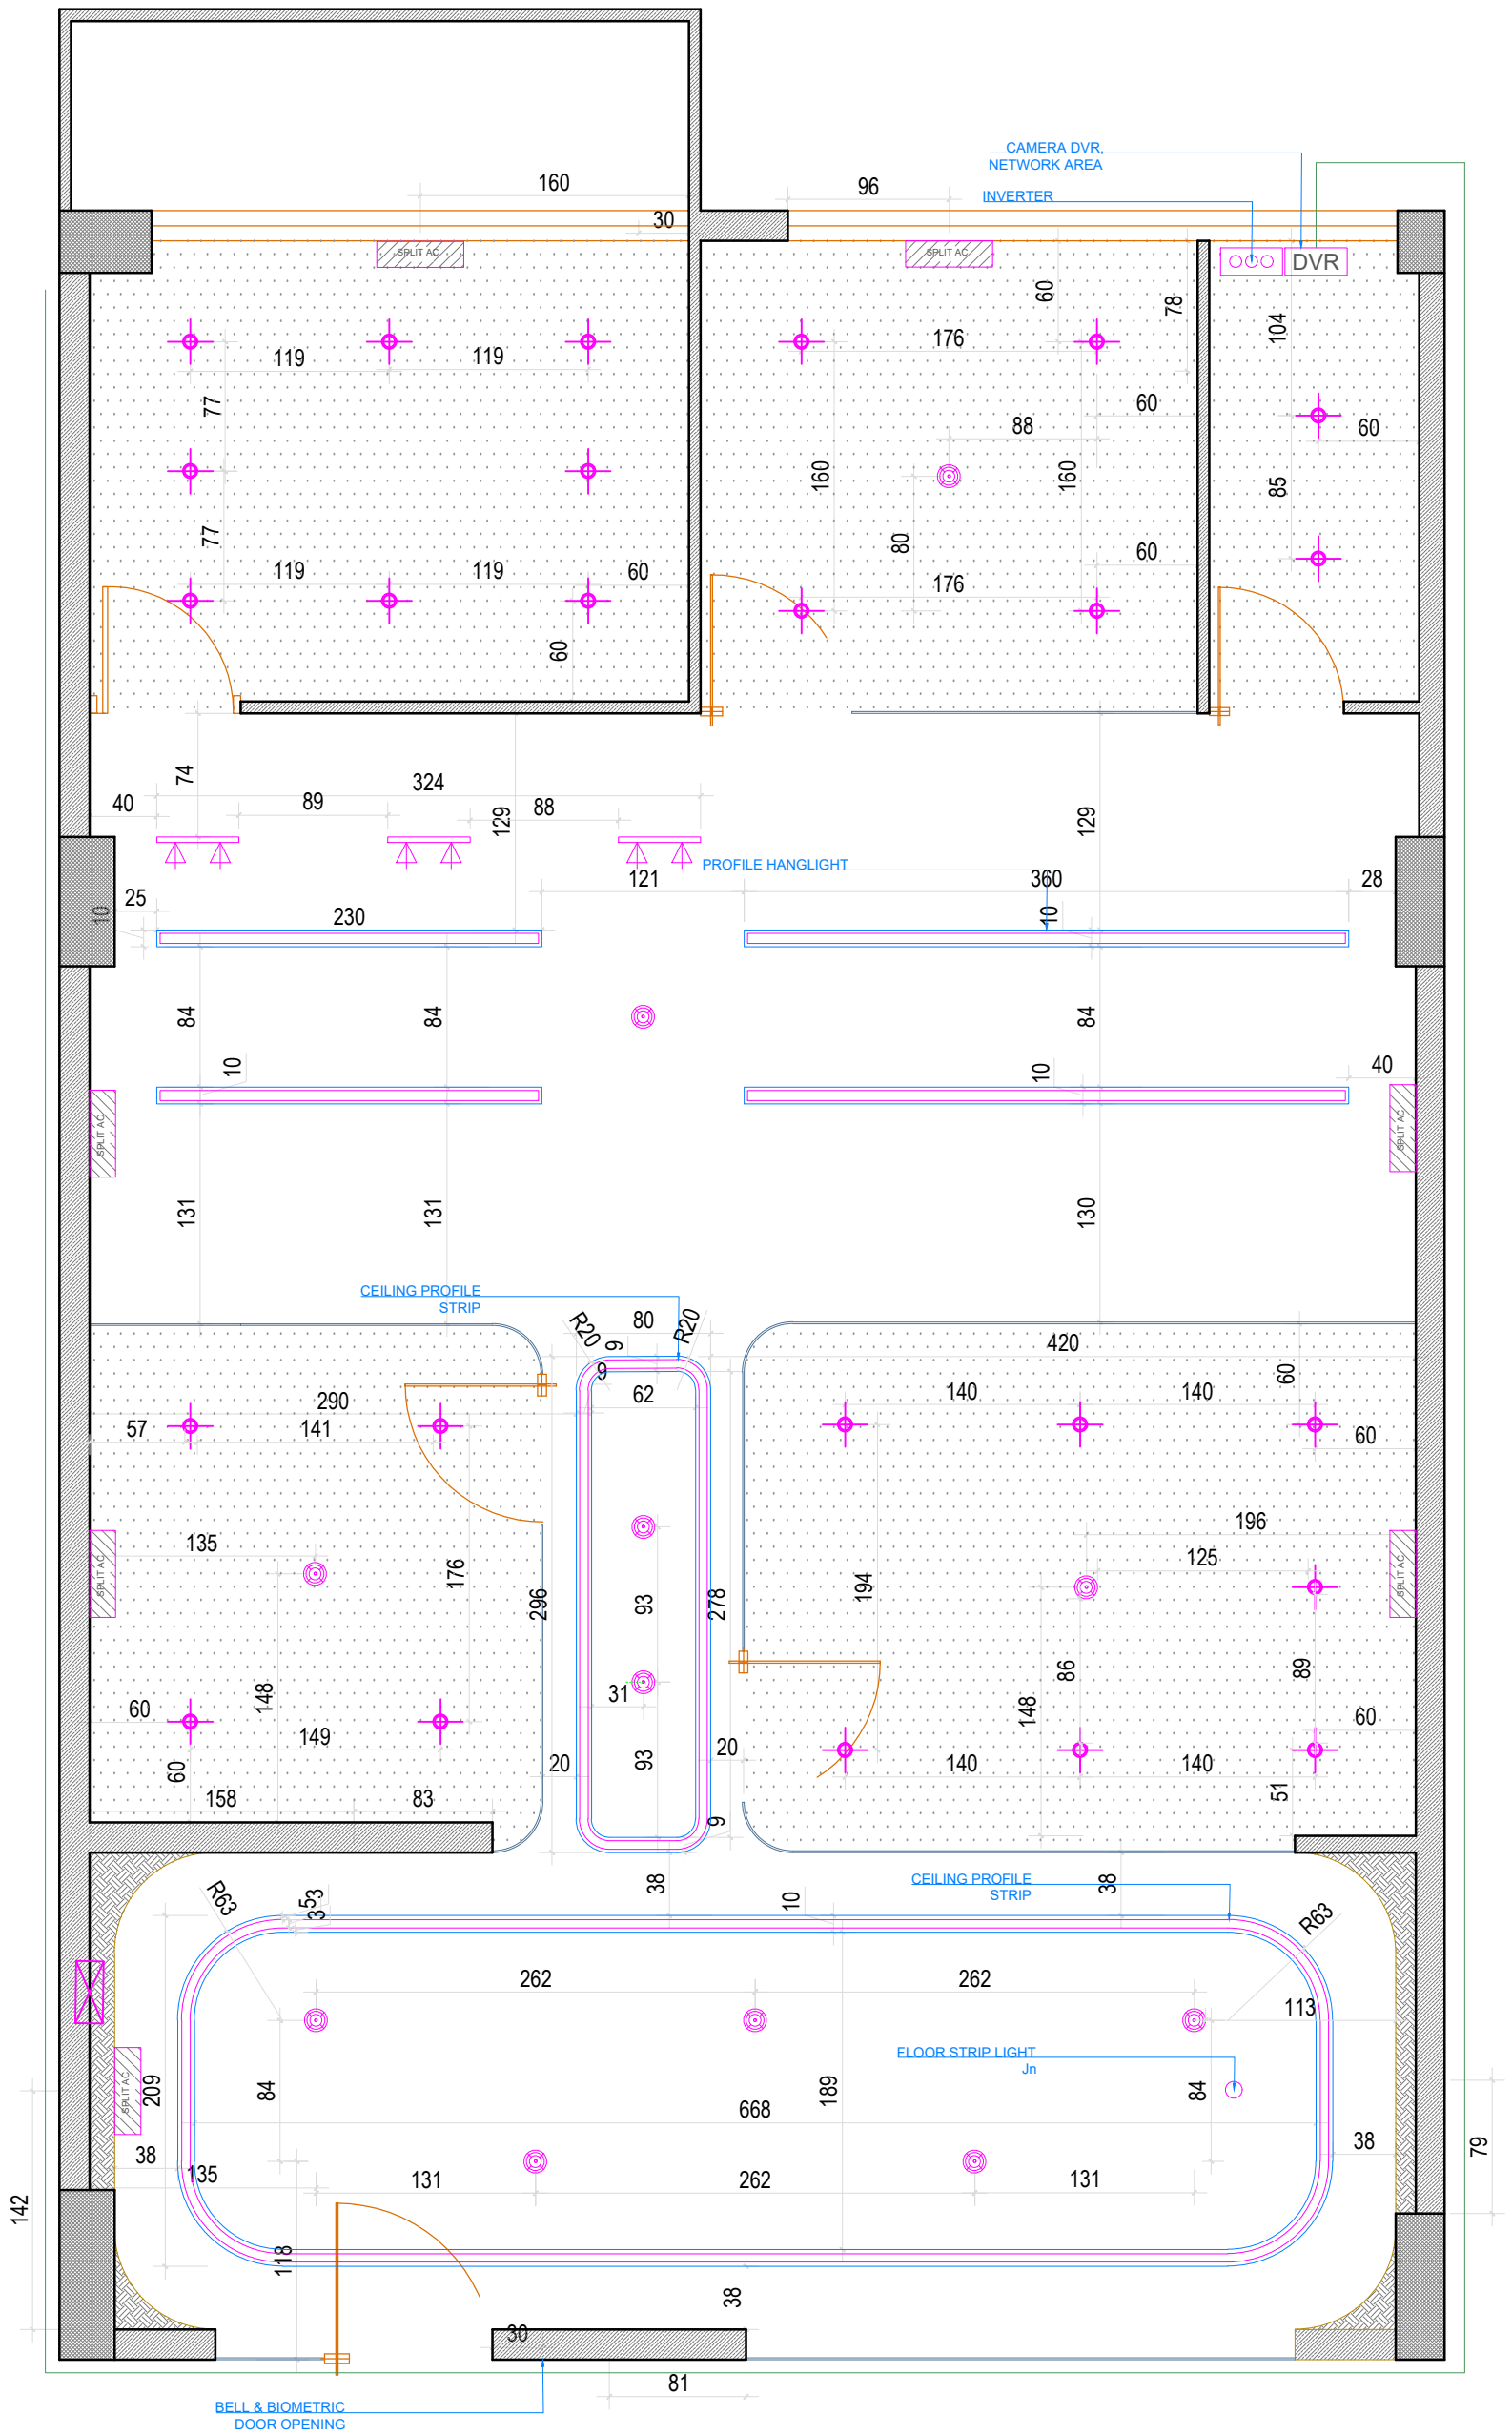

NOTES :-

* ALL MEASUREMENTS ARE IN CM UNLESS OTHERWISE SPECIFIED
* DRAWINGS NOT TO BE SCALED
* DRAWINGS TO BE READ IN CONJUNCTION AND RELEVANT ARCHITECTURAL DRAWINGS

PROJECT
KINFRA OFFICE

INTERIOR DESIGNERS
ARCHITECTURE NEXT

STRUCTURAL CONSULTANTS

MEP CONSULTANTS

TITLE
REFLECTED CEILING PLAN

CLIENT
ABID

DWG NO. :

SHEET NAME :
A3

N

Architecture Next

THIS DRAWING IS COPYRIGHT PROTECTED. IT IS THE PROPERTY OF **ARCHITECTURE NEXT.** IT IS NOT TO BE REPRODUCED, COPIED, HANDED OVER TO A THIRD PARTY OR USED FOR ANY PURPOSE OTHER THAN THAT FOR WHICH IT HAS BEEN LOANED.

DRN. : KETH

DATE : 25.04.2026

CKD. : NAP

SCALE : NTS